

Legende SIA 400


Beton	ST UK roh Sturz
Backstein (MB)	BR OK fertig Brüstung
Kalksandstein (MK)	SW OK Schwelle
Wärmedämmung	FB Fertig Boden
Beton vorfabriziert	RB Roh Boden
Leichtbau	RD Roh Decke
	NLP Nasslöschposten
	HFL Handfeuerlöscher
	BA Bodenablauf

Kante über/vor Schnittebene

Masse Türhöhen: OK fertig Boden bis UK roh Sturz

Masse Fensterhöhen: OK fertig Brüstung bis UK roh Sturz



Index	Datum	Aenderung
H	09.02.05	Deckenleuchten Treppe,Türe Medien/Sprinkler,keine Türe Sprinkler/Korridor,MK Sprinkler/Sanitär
I	24.02.05	Türhöhen bei MK Wänden geändert, Traforaum angepasst
J	19.04.05	Traforaum angepasst, Raumstempel, Vermassungen ergänzt

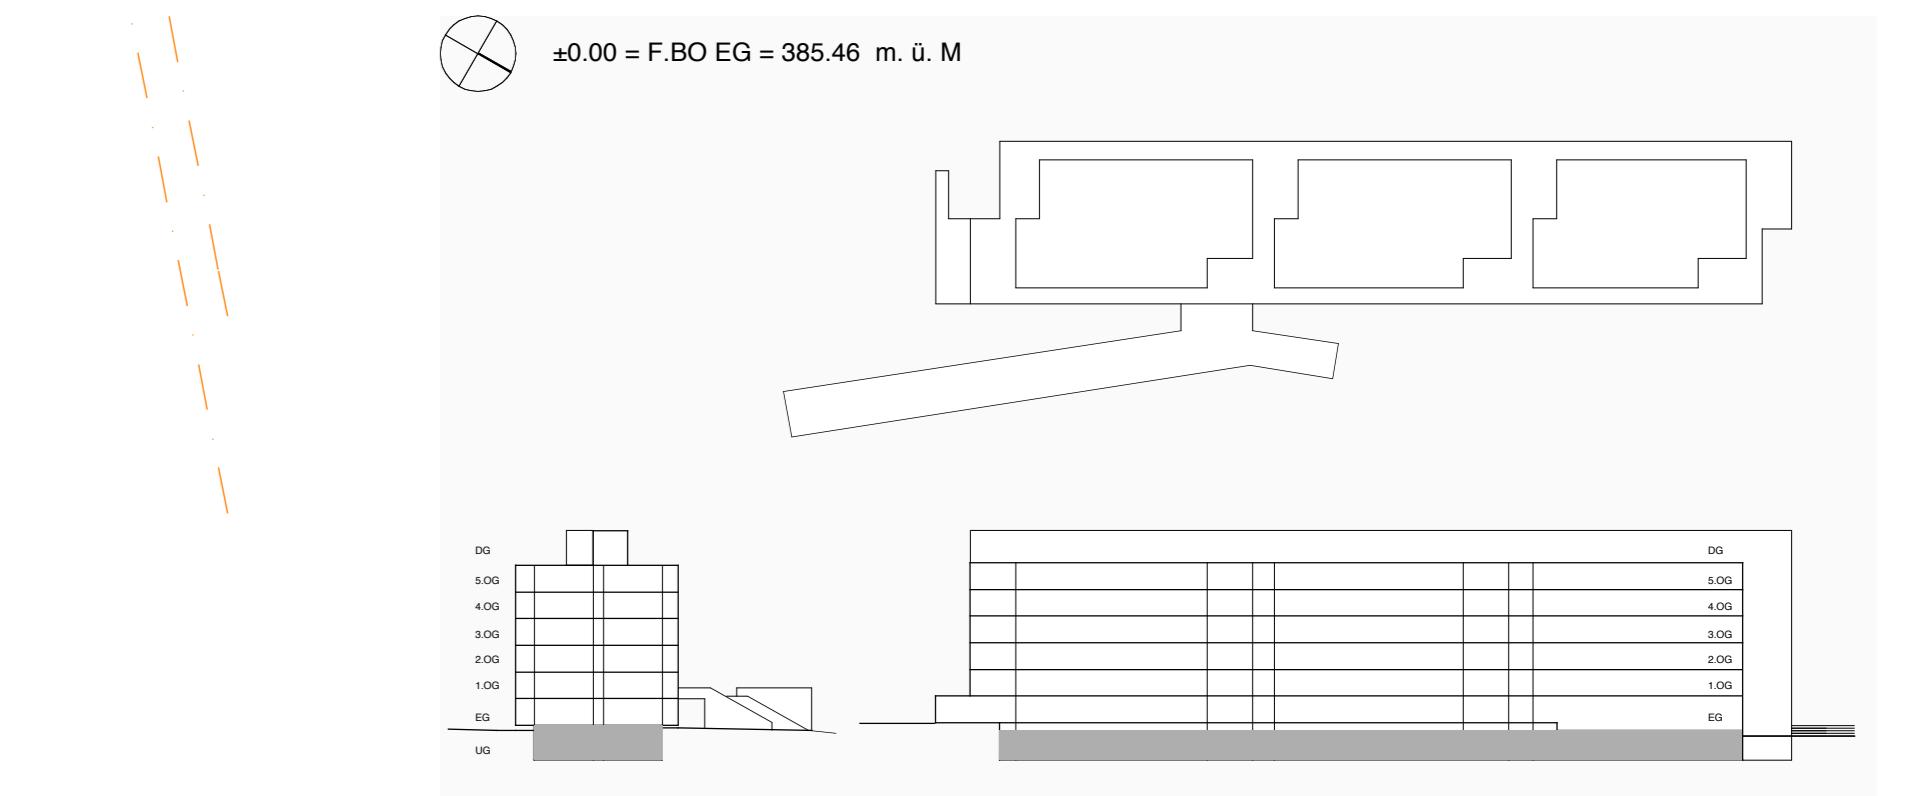



Stadt Baden, Planung und Bau, Rathausgasse 5, 5401 Baden

0212 BBB BERUFSSCHULE BERUFSBILDUNG BADEN
BBB_B SCHULHAUS BRUGGERSTRASSEB - W - 2 2 0 Untergeschoss
J Werkplan

MST. 1:100

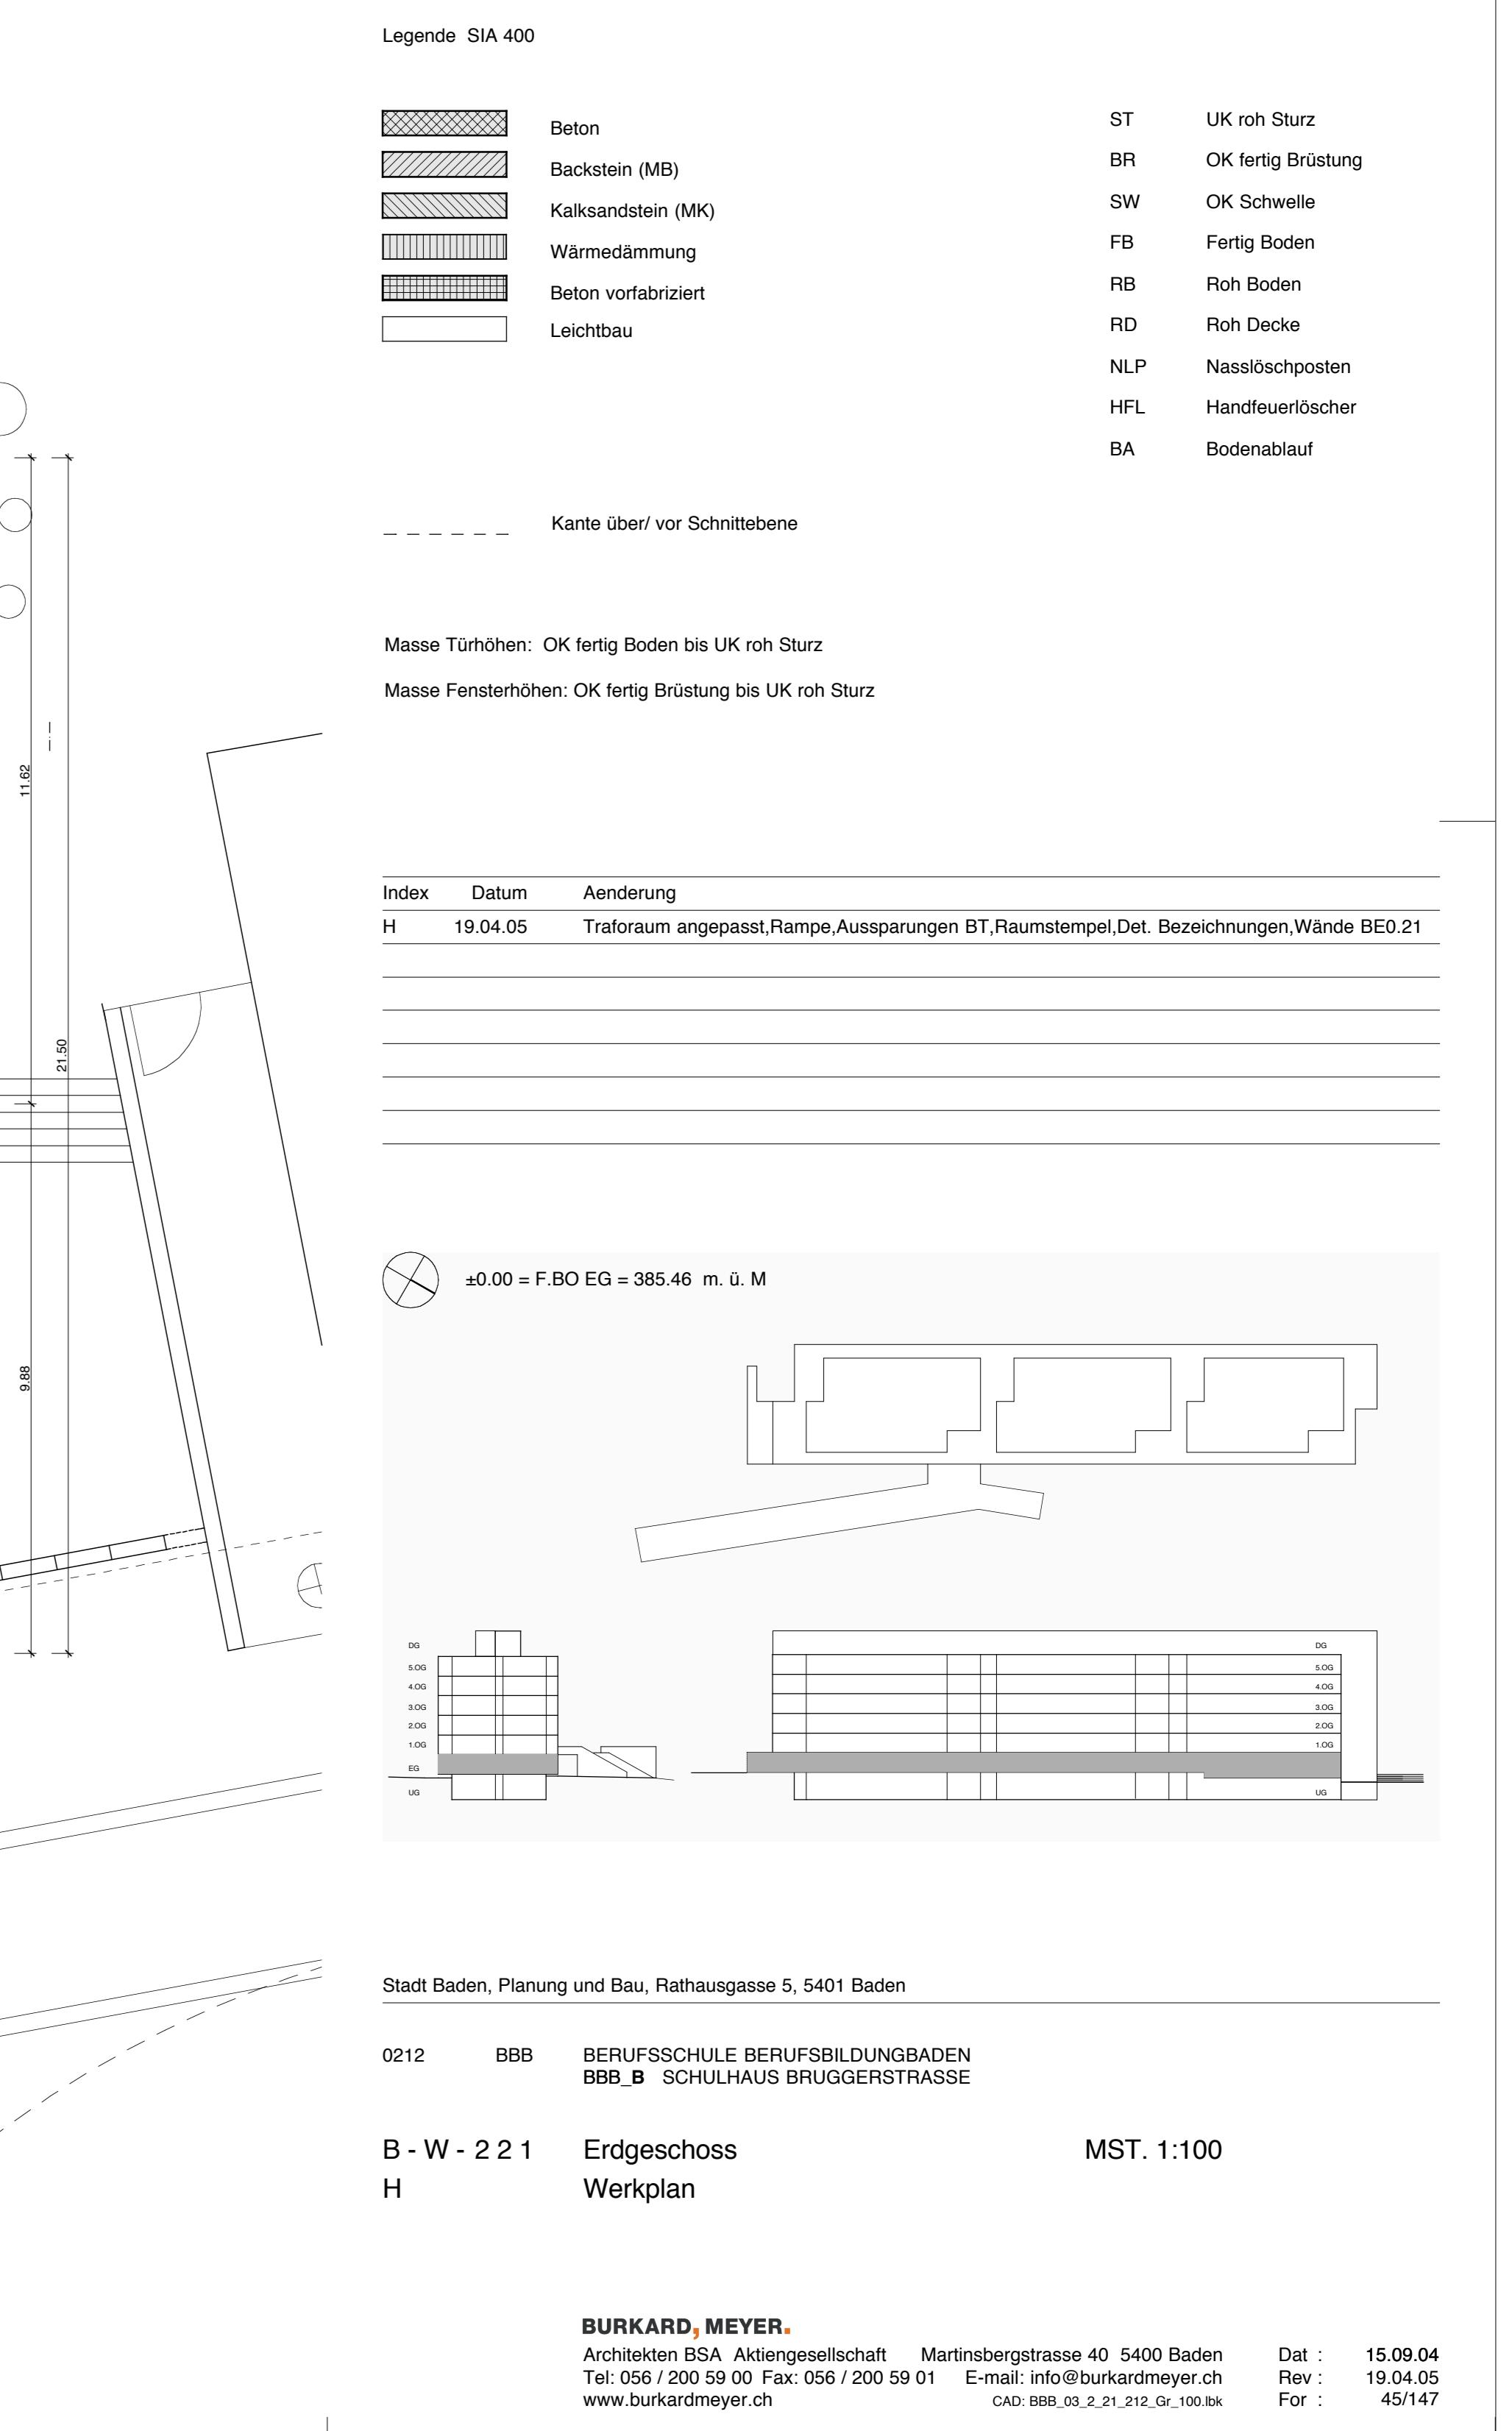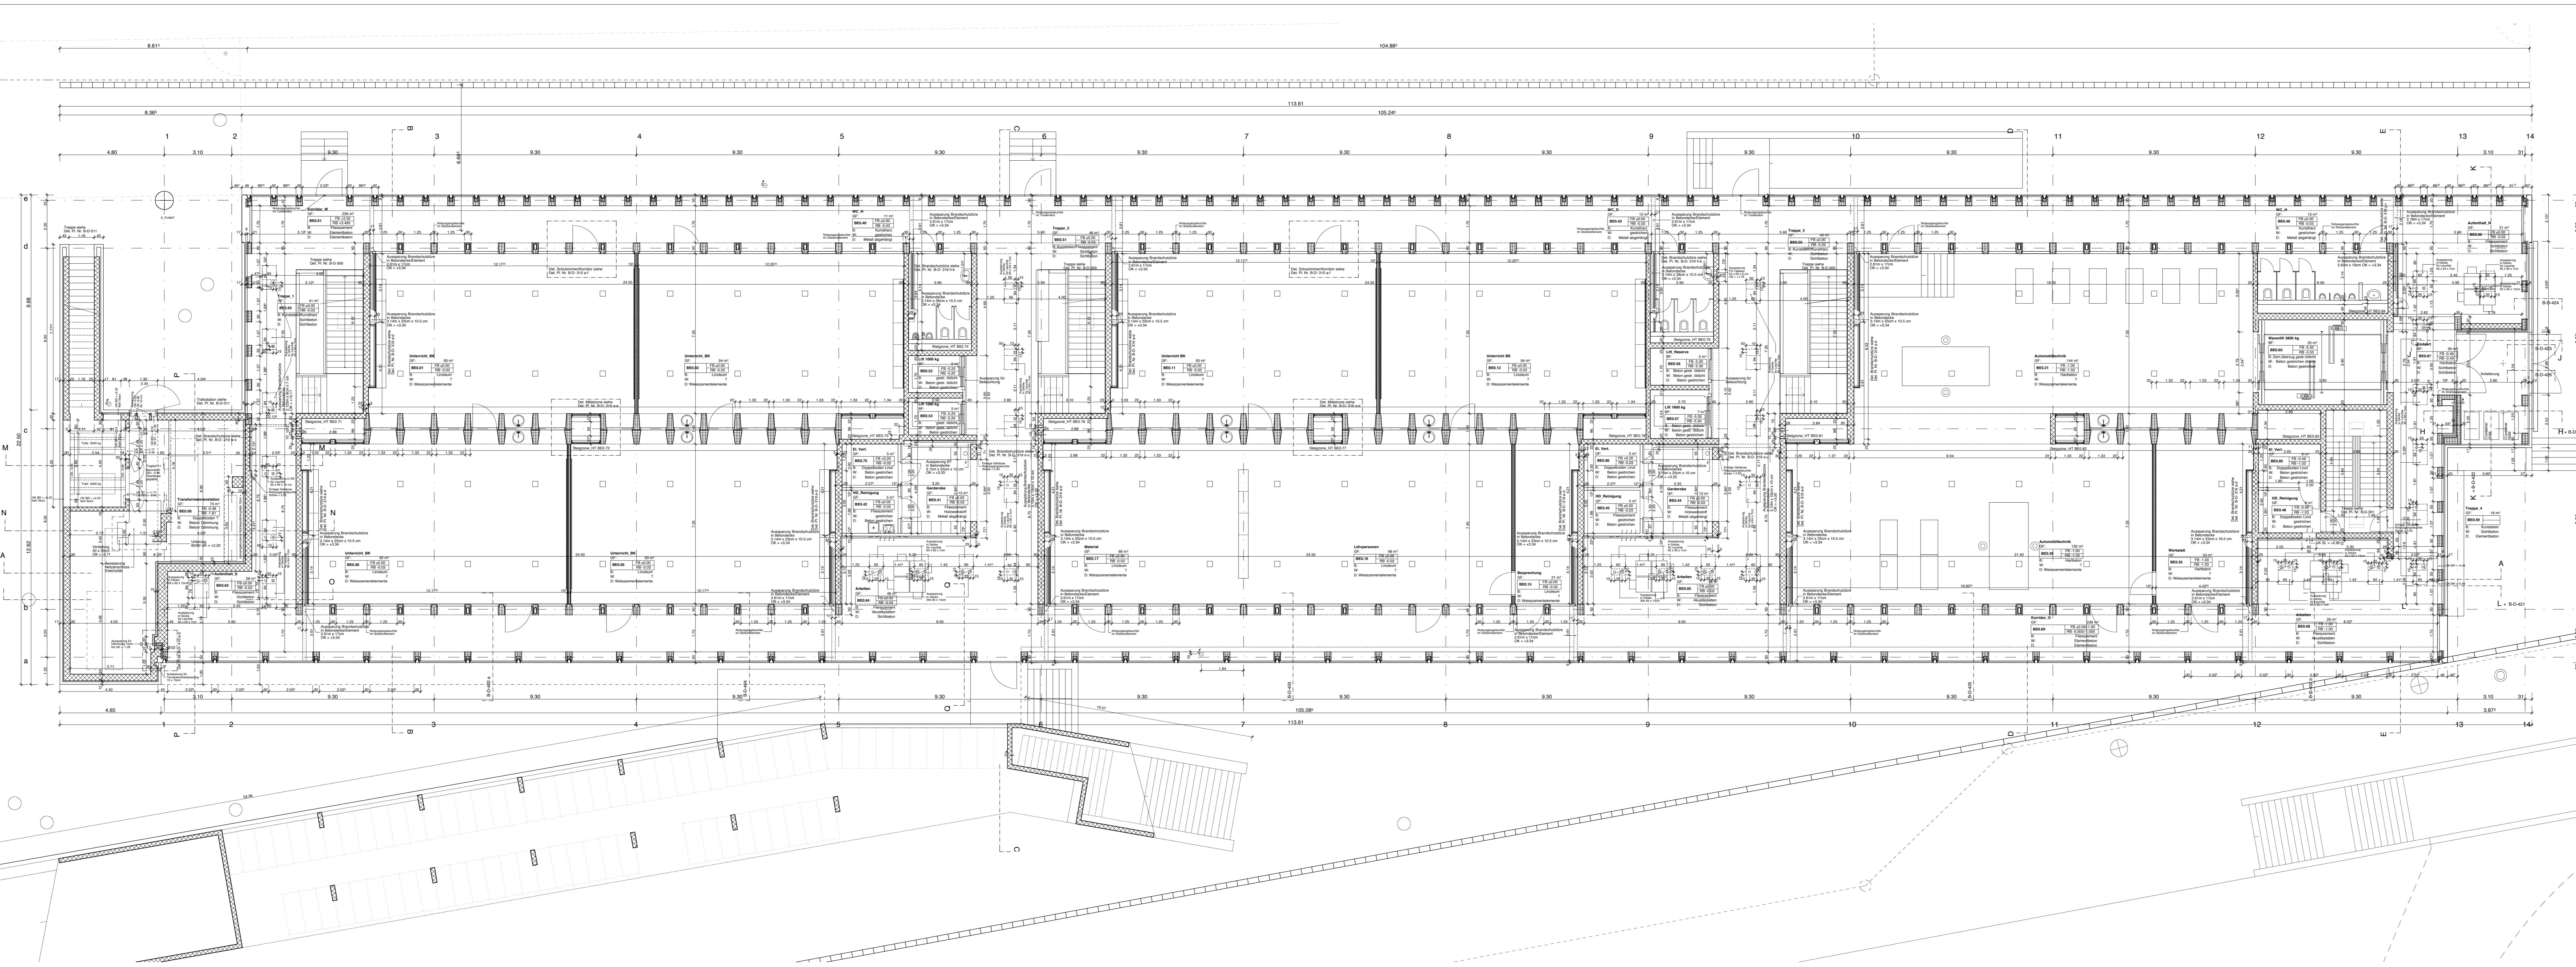

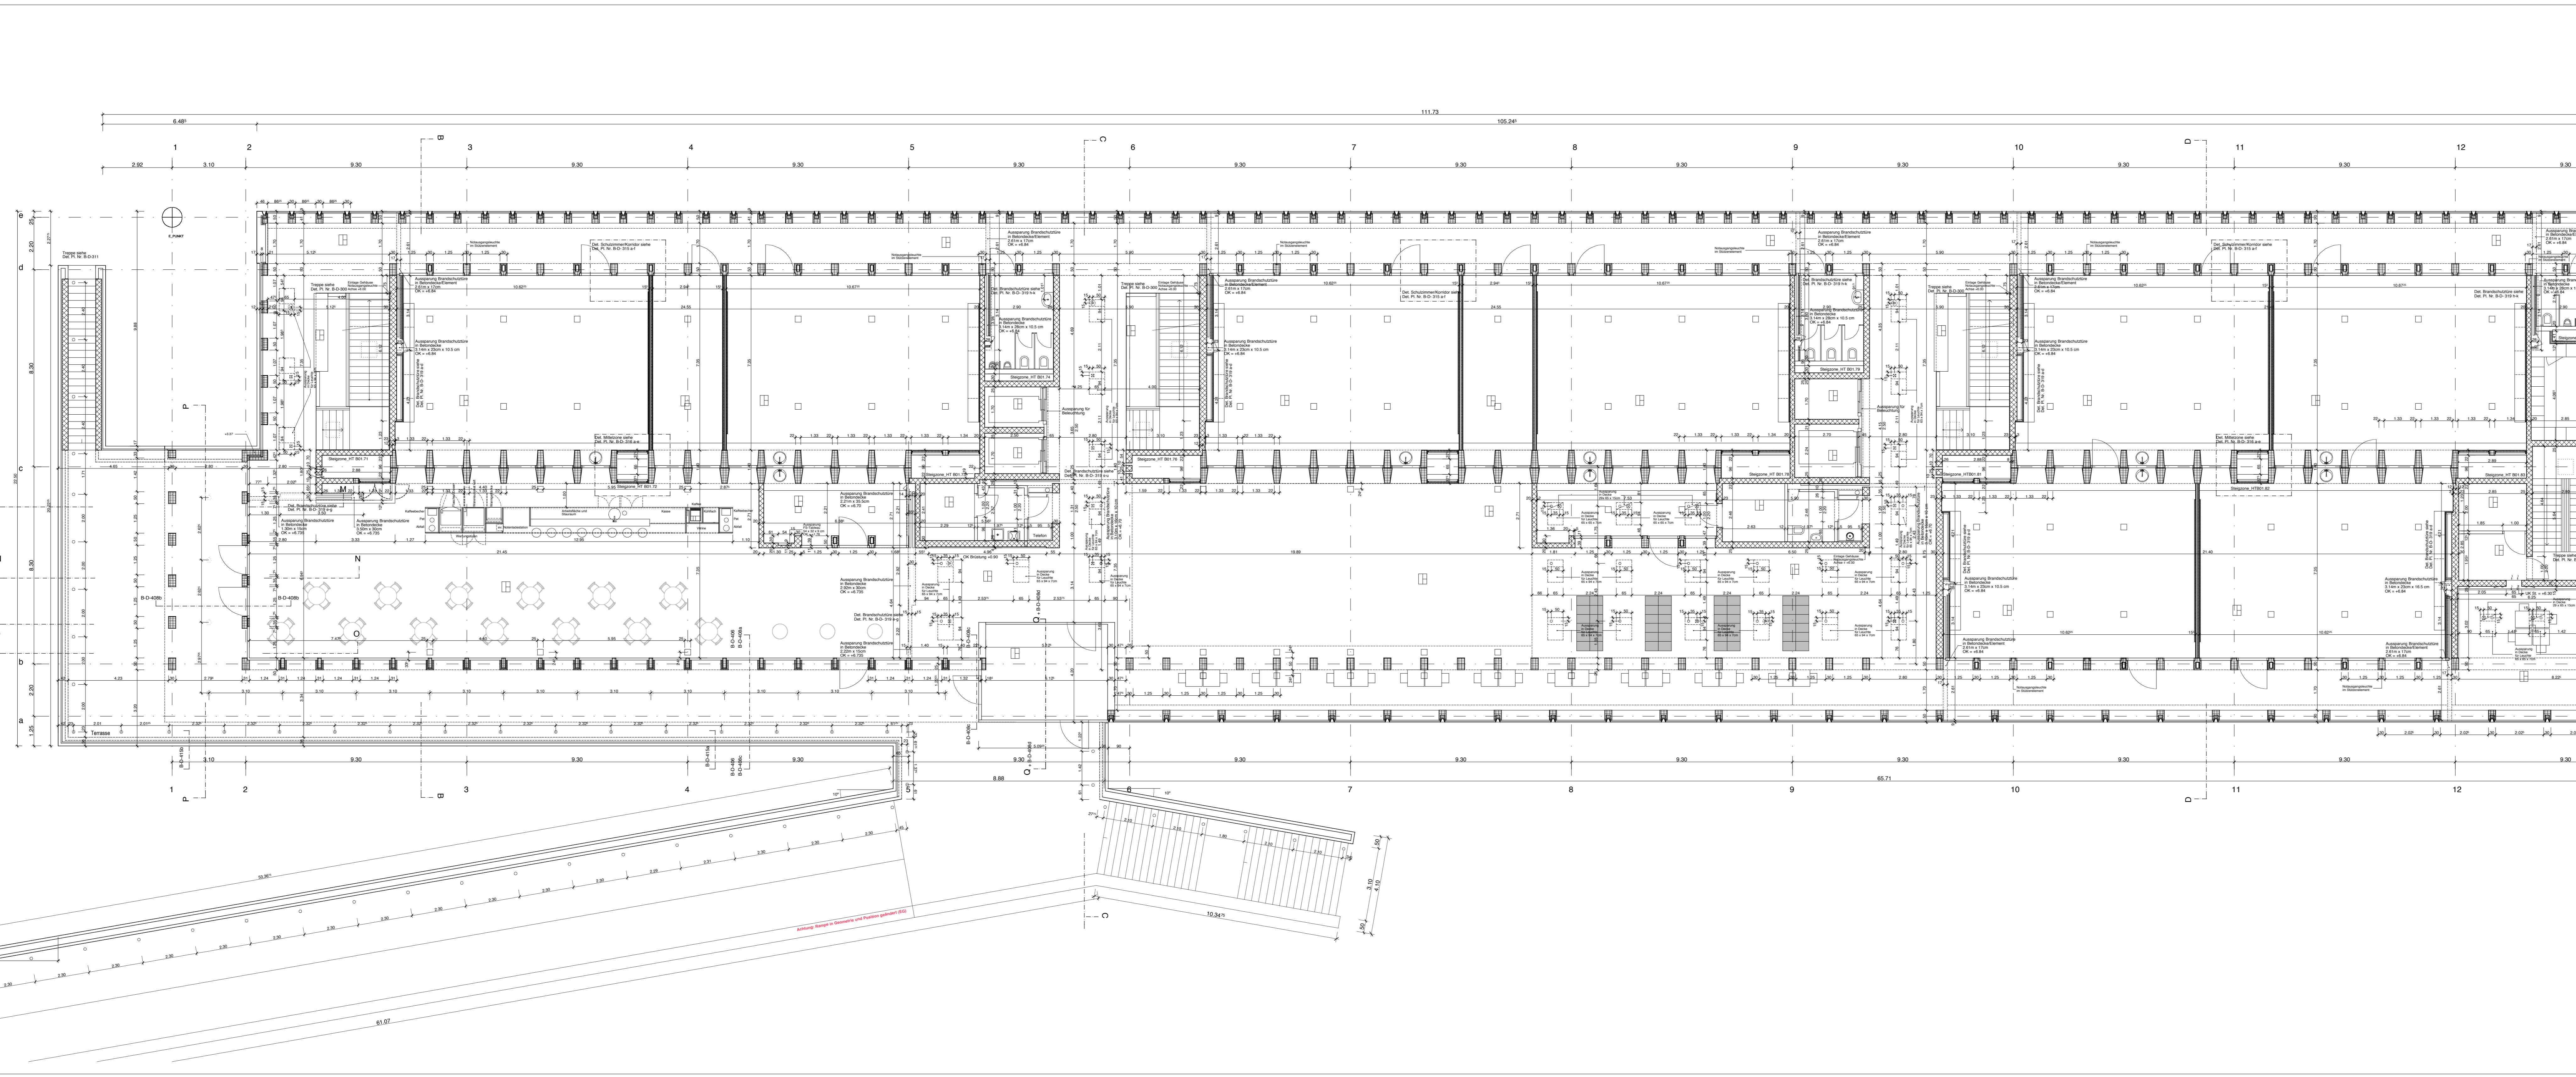

 


Stadt Baden, Planung und Bau, Rathausgasse 5, 5401 Baden

0212 BBB BERUFSSCHULE BERUFSBILDUNG BADEN
BBB_B SCHULHAUS BRUGGERSTRASSE

B - W - 2 2 3 2. Obergeschoss
Werkplan

MST. 1:100

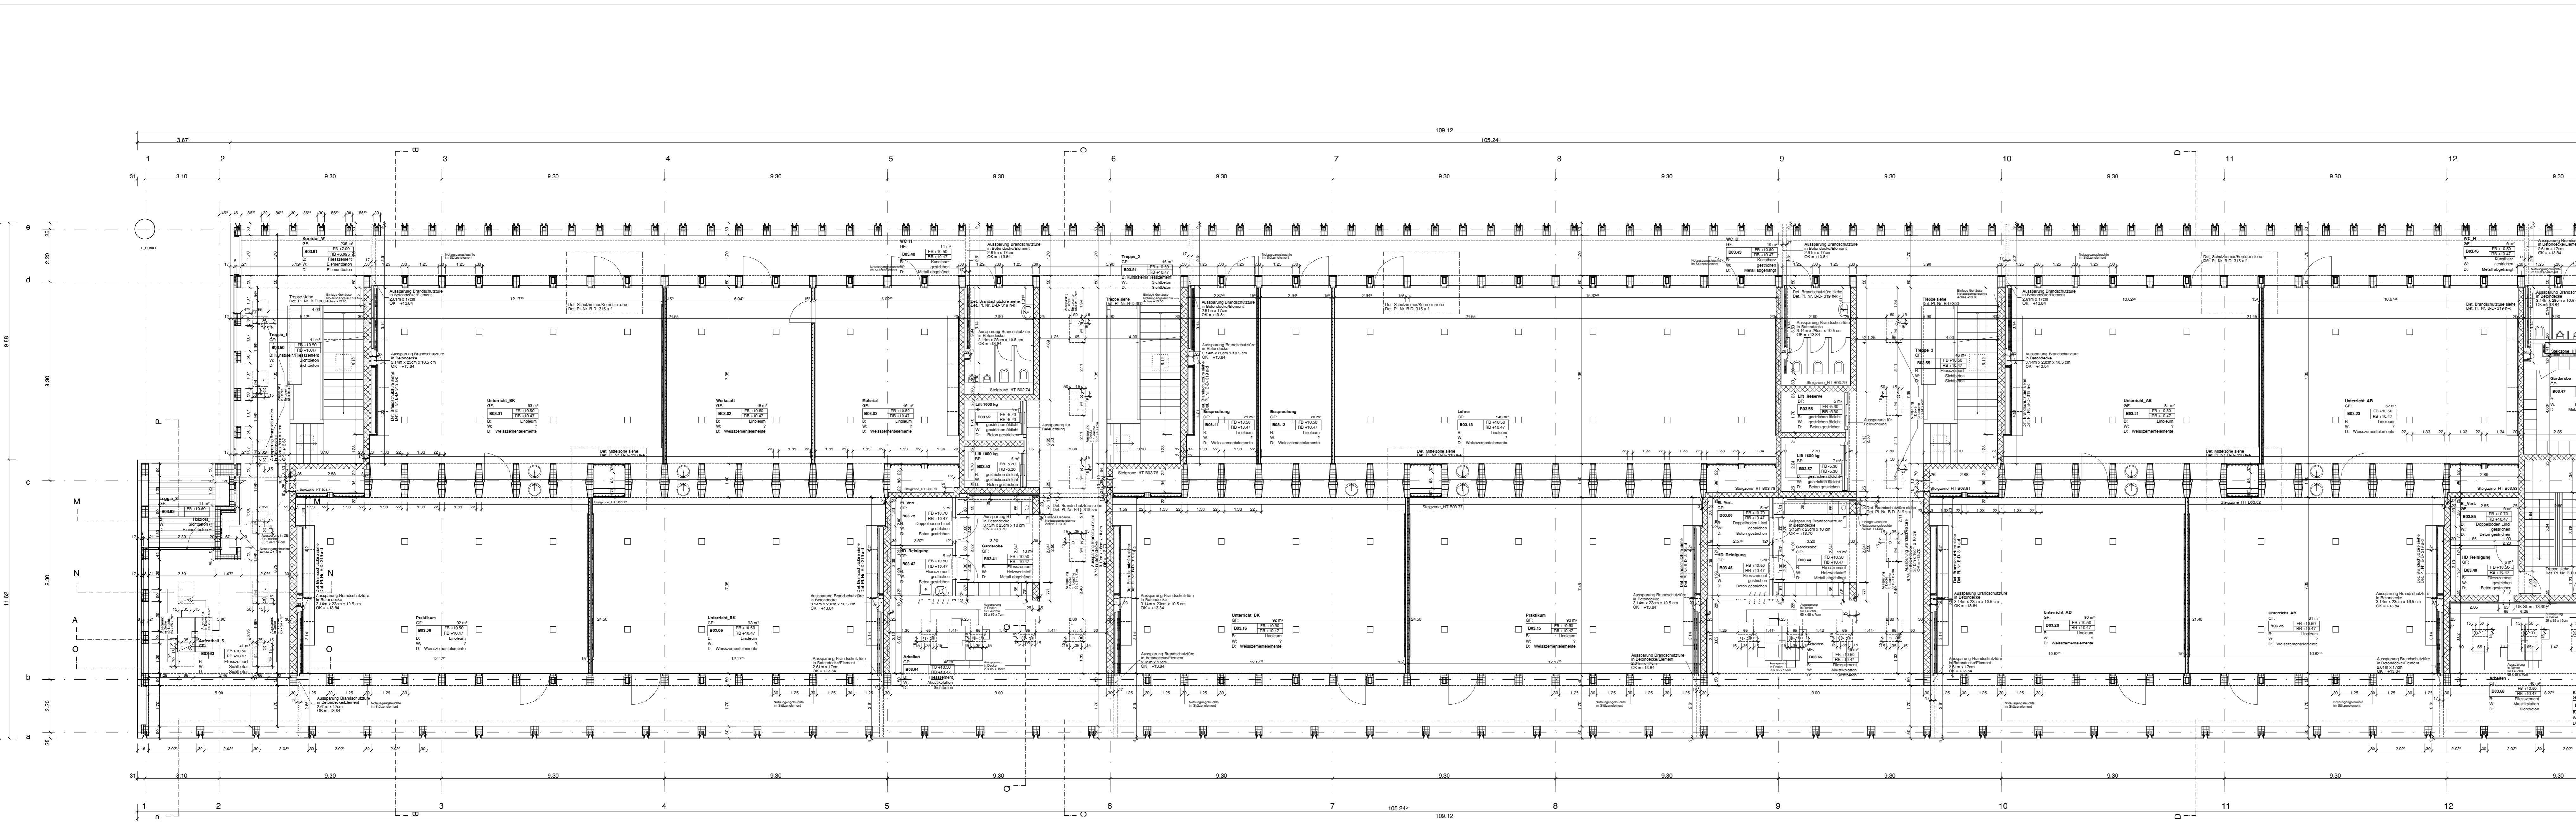

Legende SIA 400


Beton	ST UK roh Sturz
Backstein (MB)	BR OK fertig Brüstung
Kalksandstein (MK)	SW OK Schwelle
Wärmedämmung	FB Fertig Boden
Beton vorgefertigt	RB Roh Boden
Leichtbau	RD Roh Decke
	NLP Nasslöschposten
	HFL Handfeuerlöscher
	BA Bodenablauf

Kante über/vor Schnittebene

Masse Türhöhen: OK fertig Boden bis UK roh Sturz
Masse Fensterhöhen: OK fertig Brüstung bis UK roh Sturz

Index Datum Änderung
A 25.04.05 Totale Überarbeitung

$\pm 0.00 = F.O. EG = 385.46 \text{ m. ü. M}$

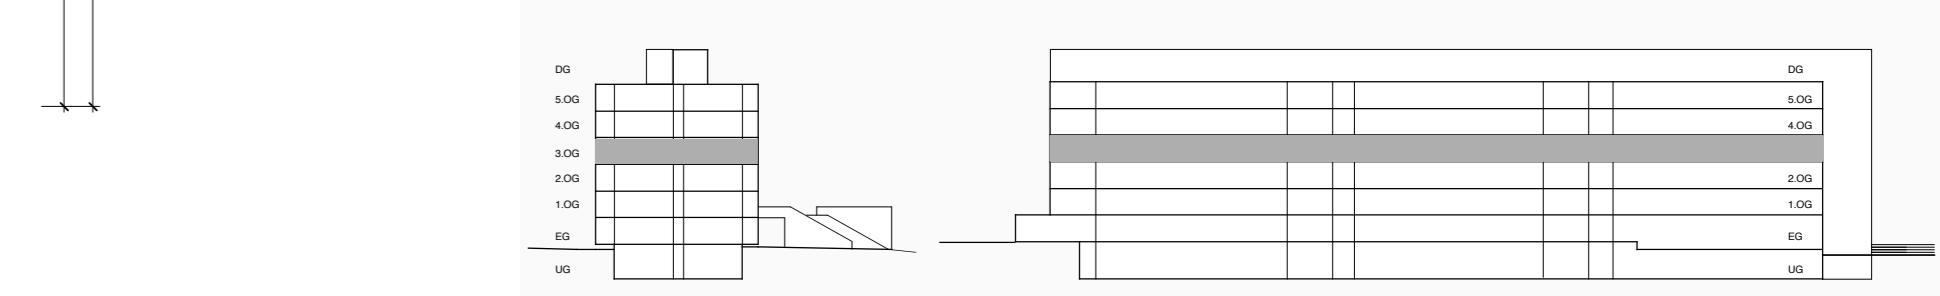


Stadt Baden, Planung und Bau, Rathausgasse 5, 5401 Baden

0212 BBB BERUFSSCHULE BERUFSBILDUNG BADEN
BBB_B SCHULHAUS BRUGGERSTRASSE

B - W - 2 2 4 3. Obergeschoss
A Werkplan MST. 1:100

BURKARD, MEYER.
Architekten BSA Aktiengesellschaft Martinsbergstrasse 40 5400 Baden Tel: 056 / 200 59 00 Fax: 056 / 200 59 01 E-mail: info@burkardmeyer.ch Rev : 24.08.04
www.burkardmeyer.ch CAD BBB_03_21_212_Gr.100.lsk For : 45/147

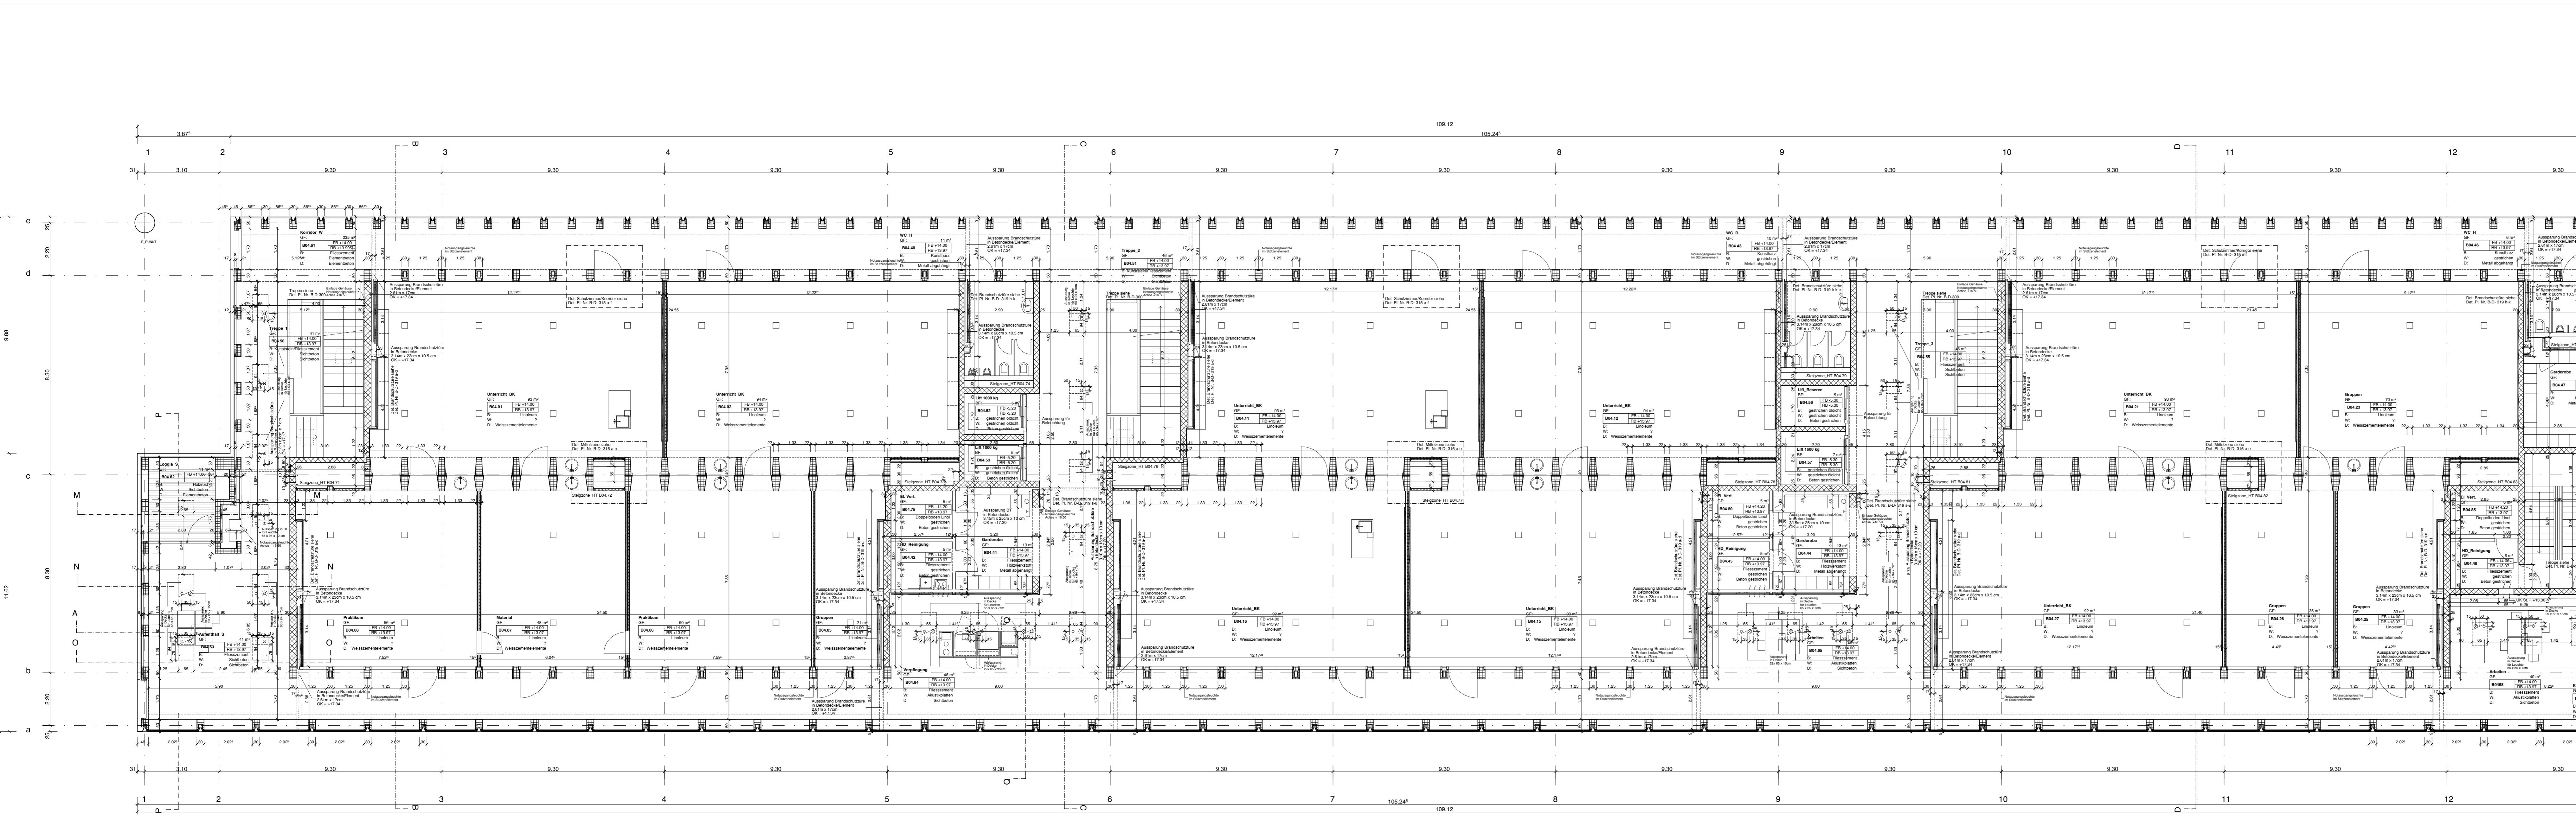


Legende SIA 400

Beton	ST UK roh Sturz
Backstein (MB)	BR OK fertig Brüstung
Kalksandstein (MK)	SW OK Schwelle
Wärmedämmung	FB Fertig Boden
Beton vorfabriziert	RB Roh Boden
Leichtbau	RD Roh Decke
	NLP Nasslöschposten
	HFL Handfeuerlöscher
	BA Bodenablauf

Kante über/vor Schnittebene
Masse Türhöhen: OK fertig Boden bis UK roh Sturz
Masse Fensterhöhen: OK fertig Brüstung bis UK roh Sturz


Index Datum Änderung
A 02.05.05 Totale Überarbeitung

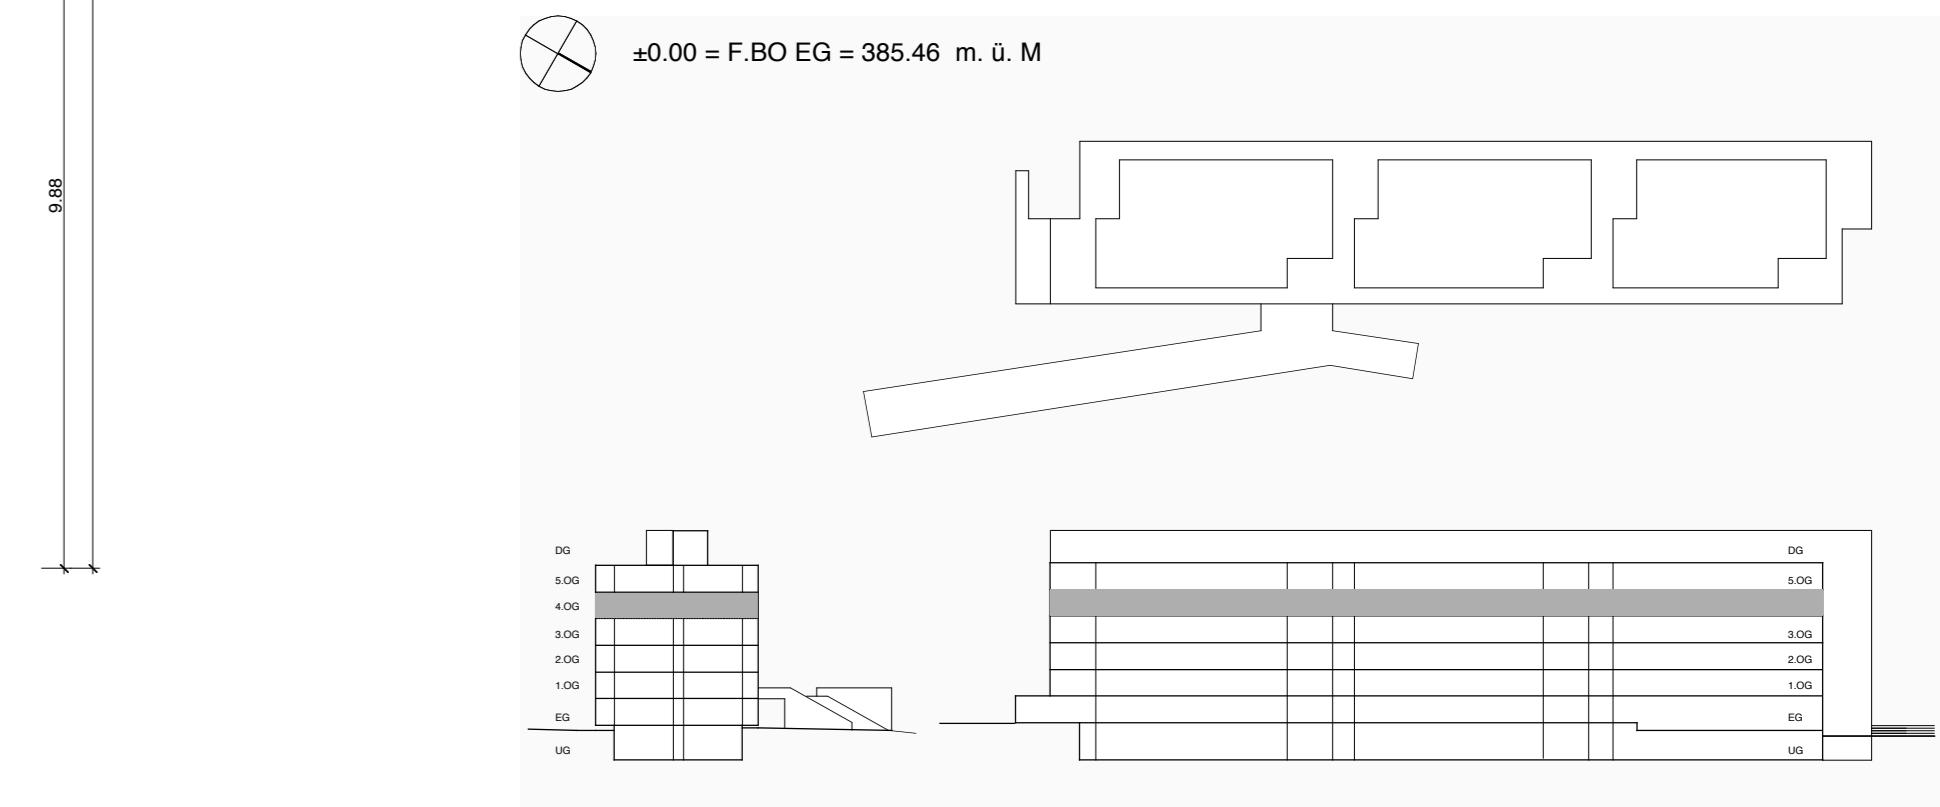

Stadt Baden, Planung und Bau, Rathausgasse 5, 5401 Baden

0212 BBB BERUFSSCHULE BERUFSBILDUNGSBADEN
BBB_B SCHULHAUS BRUGGERSTRASSE

B - W - 2 2 5 4. Obergeschoss
A Werkplan MST. 1:100

 


Stadt Baden, Planung und Bau, Rathausgasse 5, 5401 Baden

0212 BBB BERUFSCHULE BERUFSBILDUNGSBADEN
 BBB_B SCHULHAUS BRUGGERSTRASSE

B - W - 226 5. Obergeschoss
 Werkplan

MST. 1:100

 

Stadt Baden, Planung und Bau, Rathausgasse 5, 5401 Baden

0212 BBB BERUFSSCHULE BERUFSBILDUNG BADEN
 BBB_B SCHULHAUS BRUGGERSTRASSE

B - W - 2 2 7 Dachgeschoss
 D Werkplan

MST. 1:100

BURKARD, MEYER.
 Architekten BSA Aktiengesellschaft Martinsbergstrasse 40 5400 Baden Tel : 056 / 200 59 00 Fax: 056 / 200 59 01 E-mail: info@burkardmeyer.ch Rev : 15.09.04
 www.burkardmeyer.ch CAD: BBB_03_21_212_Gr_100.sk For : 45/147